


1430 NE 65th Street
Seattle, WA 98115
t: 206-322-1732
fora.land

Fora Landscape Arch


SHEET TITLE

OVERALL TREE PLAN

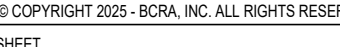

DESIGN DEVELOPMENT SET

IF SHEET MEASURES LESS THAN 30"x42", IT IS A REDUCED PRINT. REDUCE SCALE ACCORDINGLY.

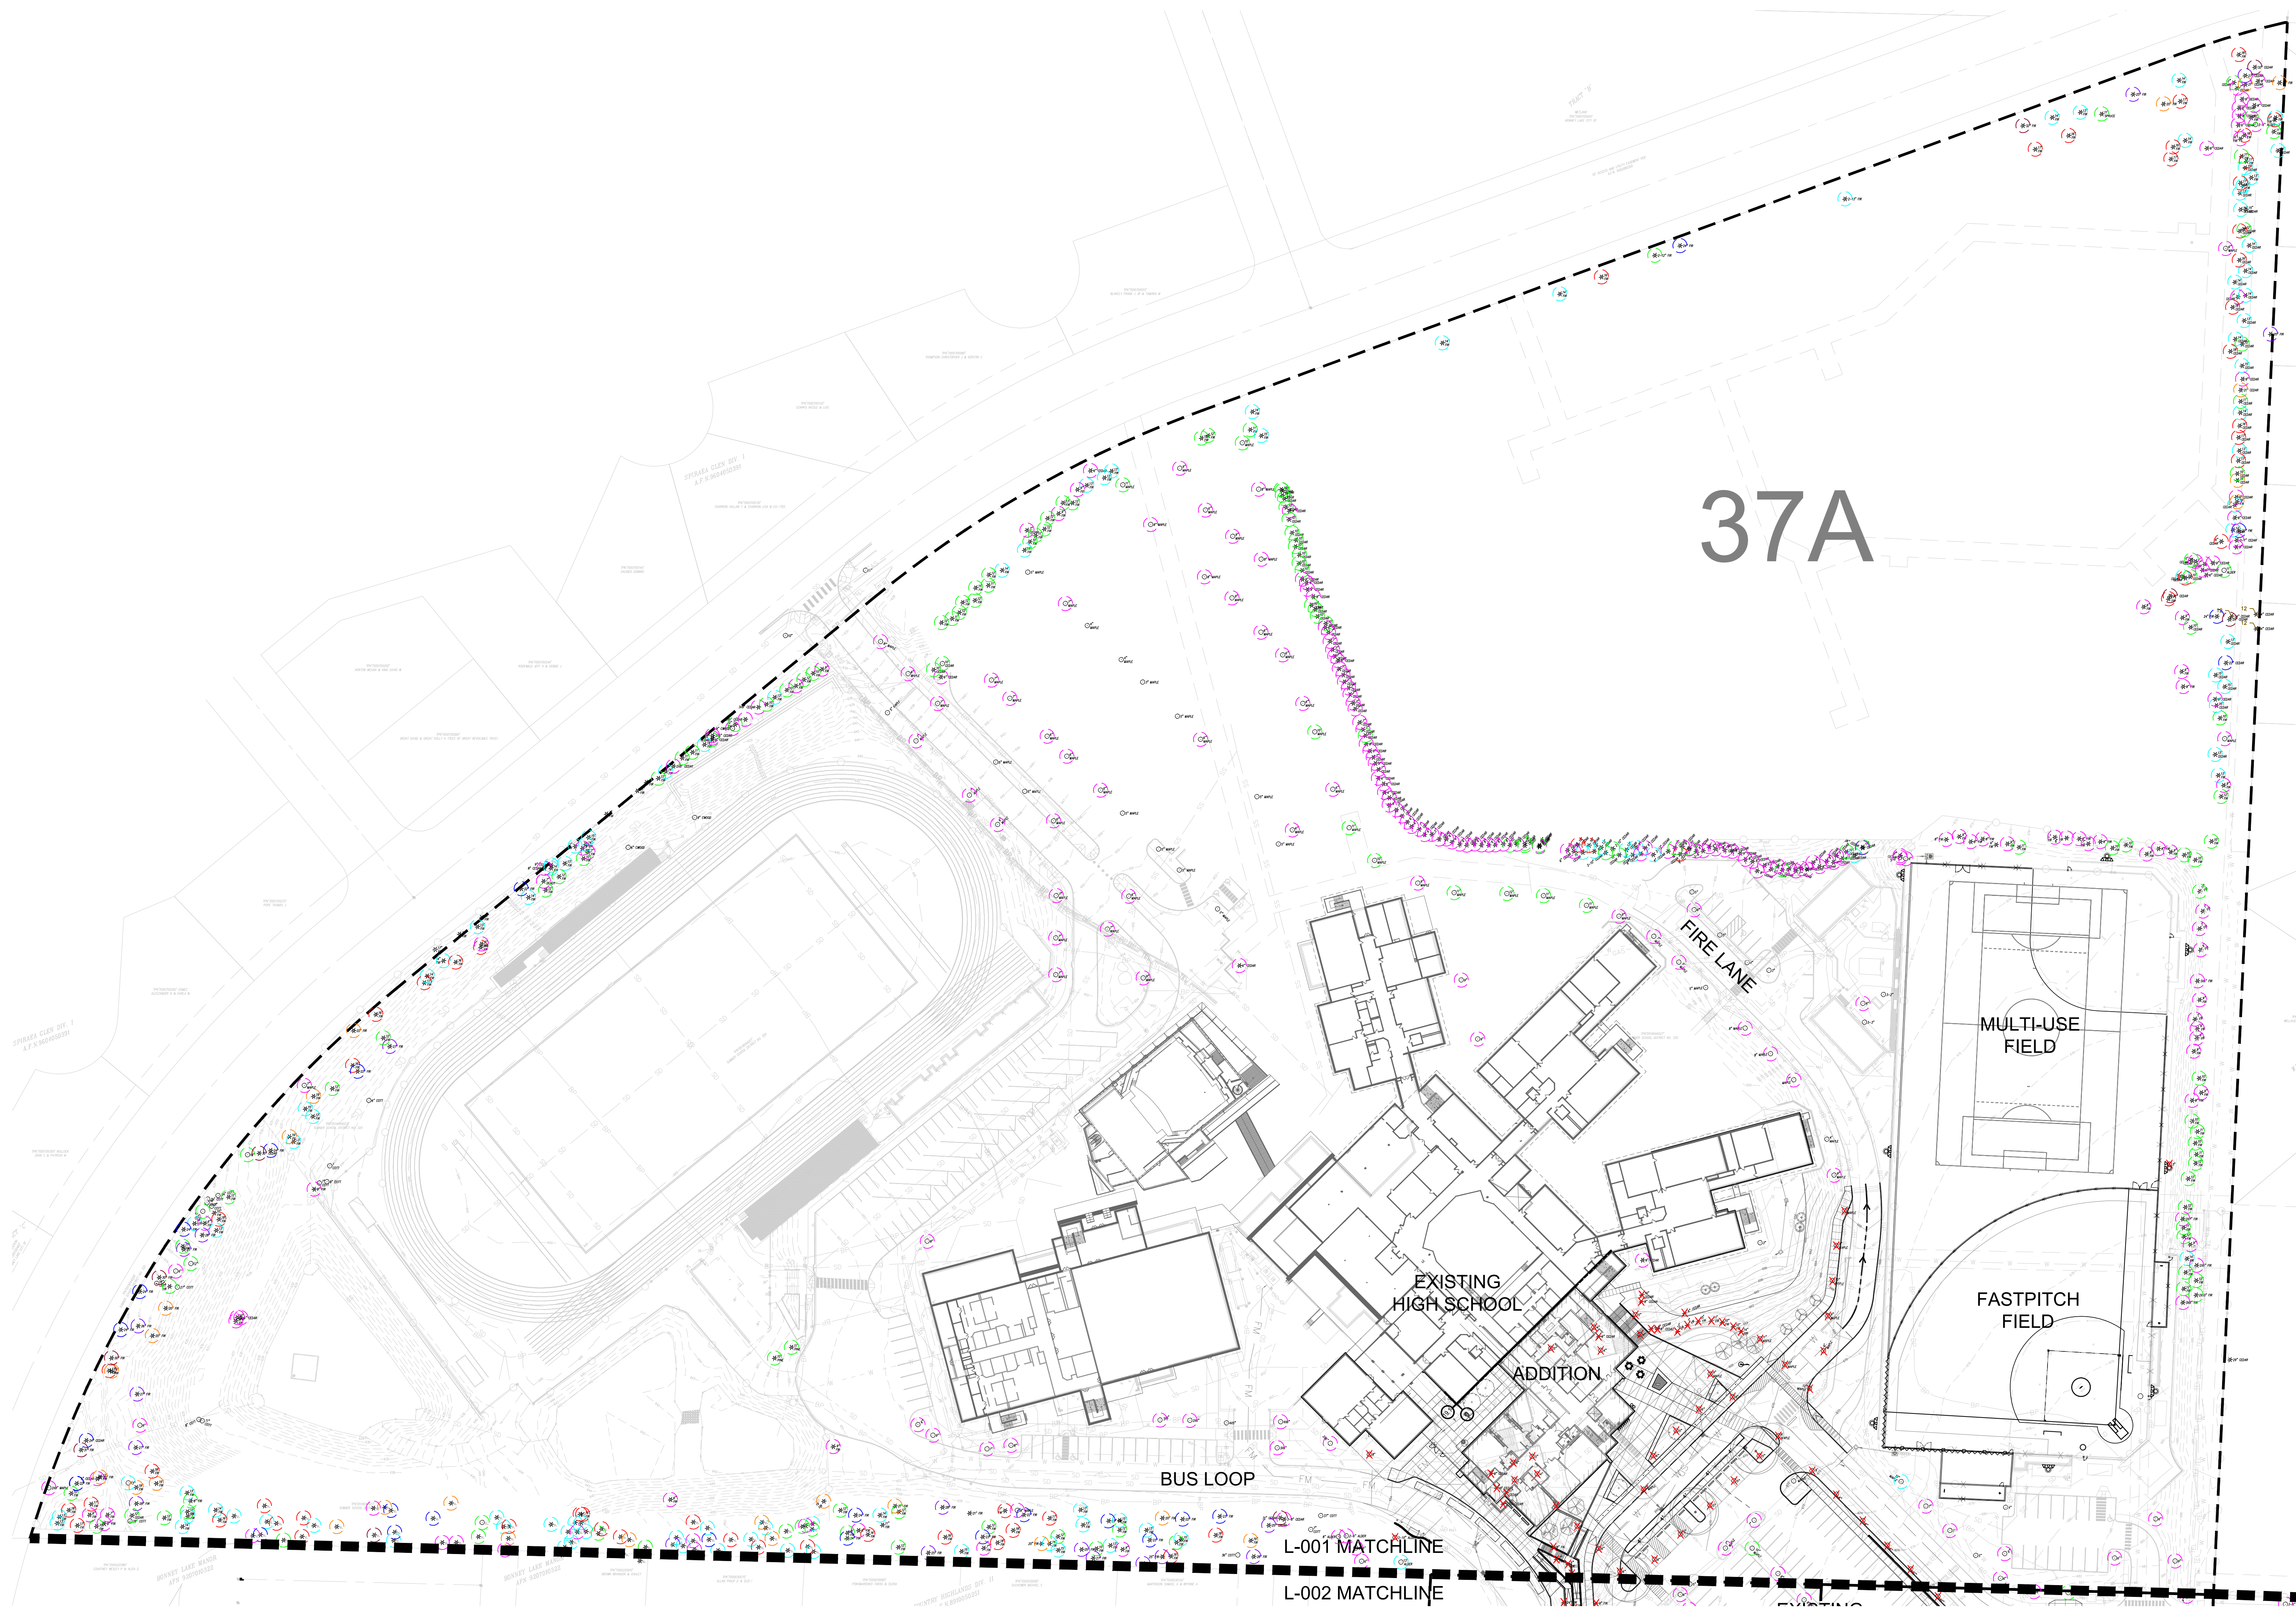

37A

EXISTING
HIGH SCHOOL

ADDITION

BUS LOOP

FIRE LANE

MULTI-USE
FIELD


FASTPITCH
FIELD

L-001 MATCHLINE

L-002 MATCHLINE

SCALE: 1"=60'-0"

0' 30' 60' 120' 240'

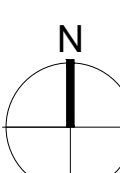



BONNEY LAKE HIGH SCHOOL EXPANSION
10920 199TH AVE CT E
BONNEY LAKE, WA 98391

26

CR, KH, PF

BY: AR

 **bcra**
© 2025 - BCRA, INC. ALL RIGHTS RESERVED

-002

